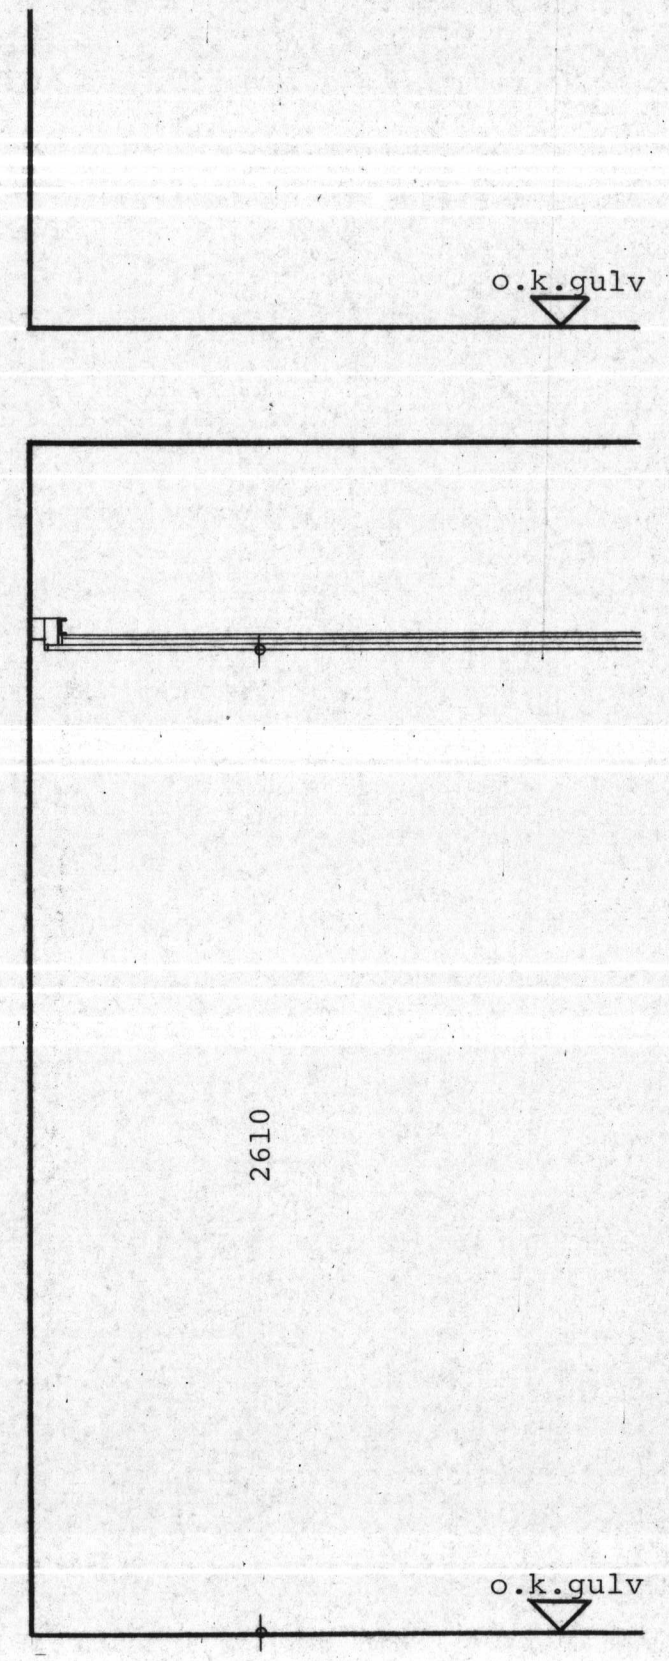

snit, 1:20

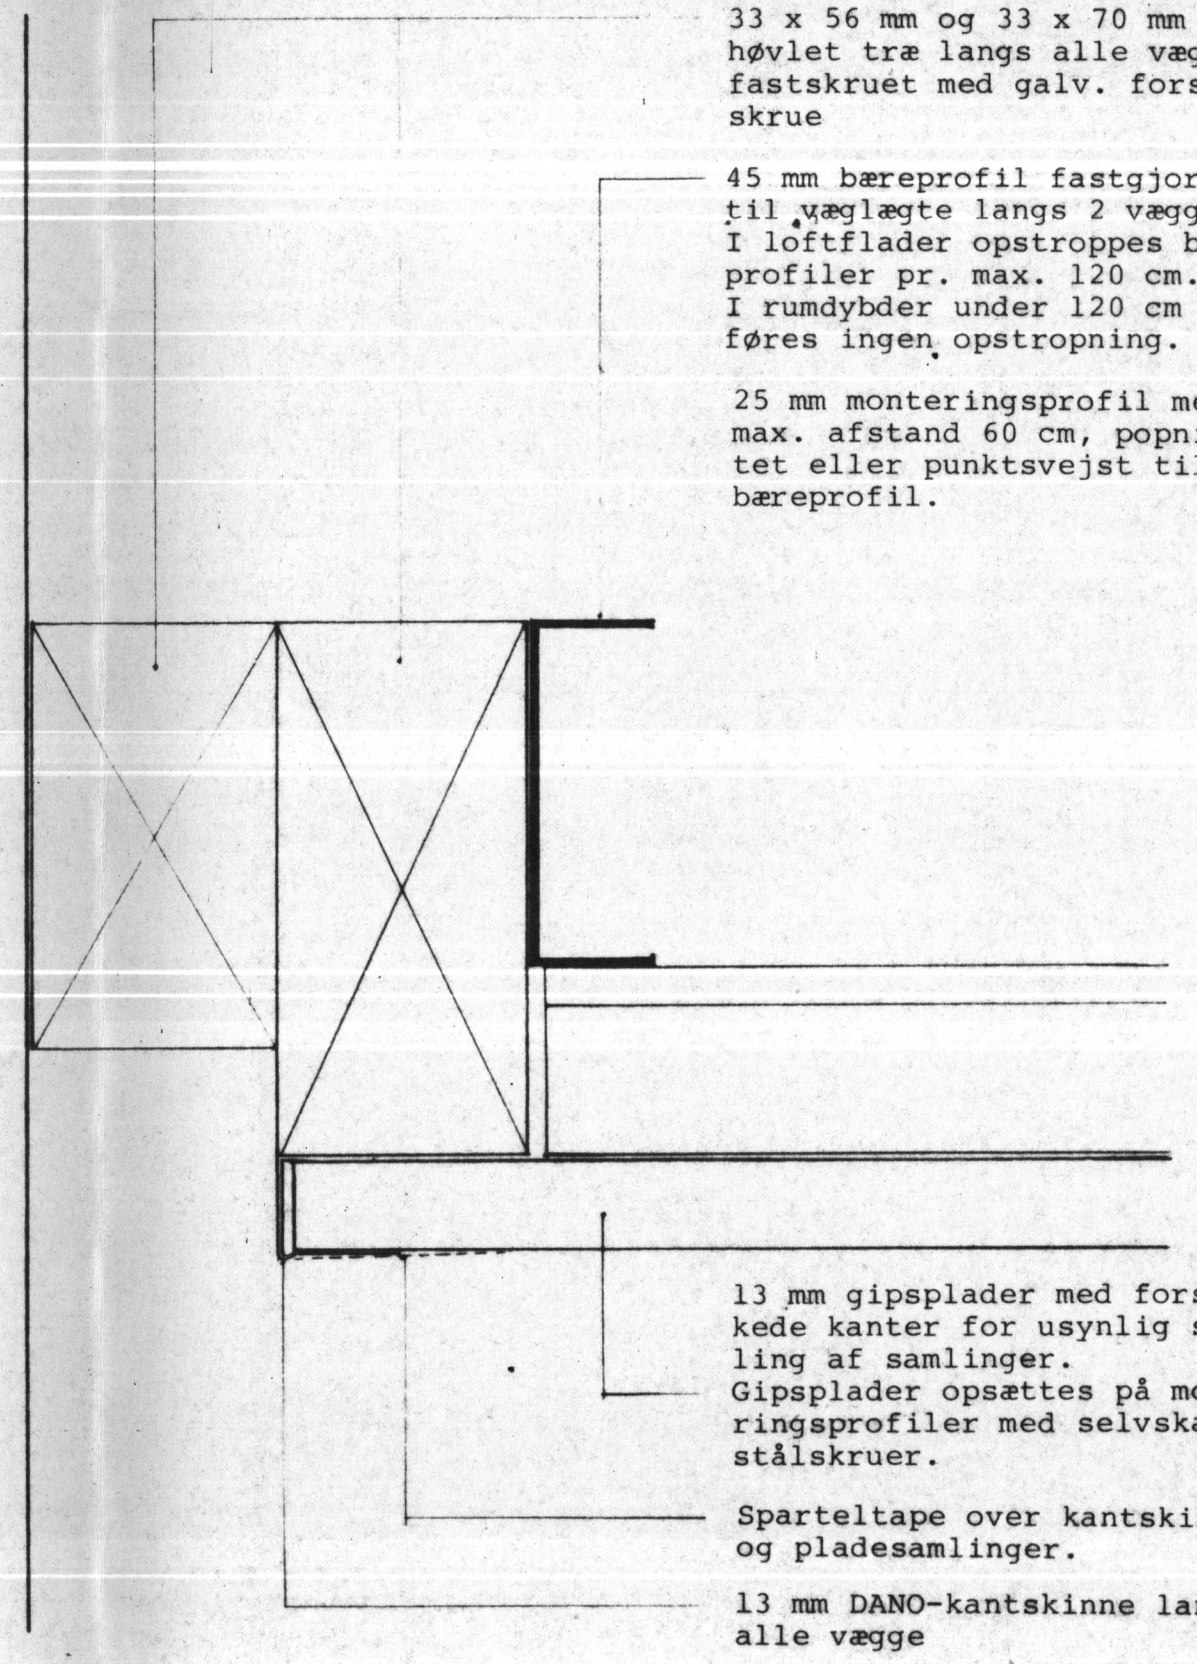

detalje af tilslutning ved væg, 1:1

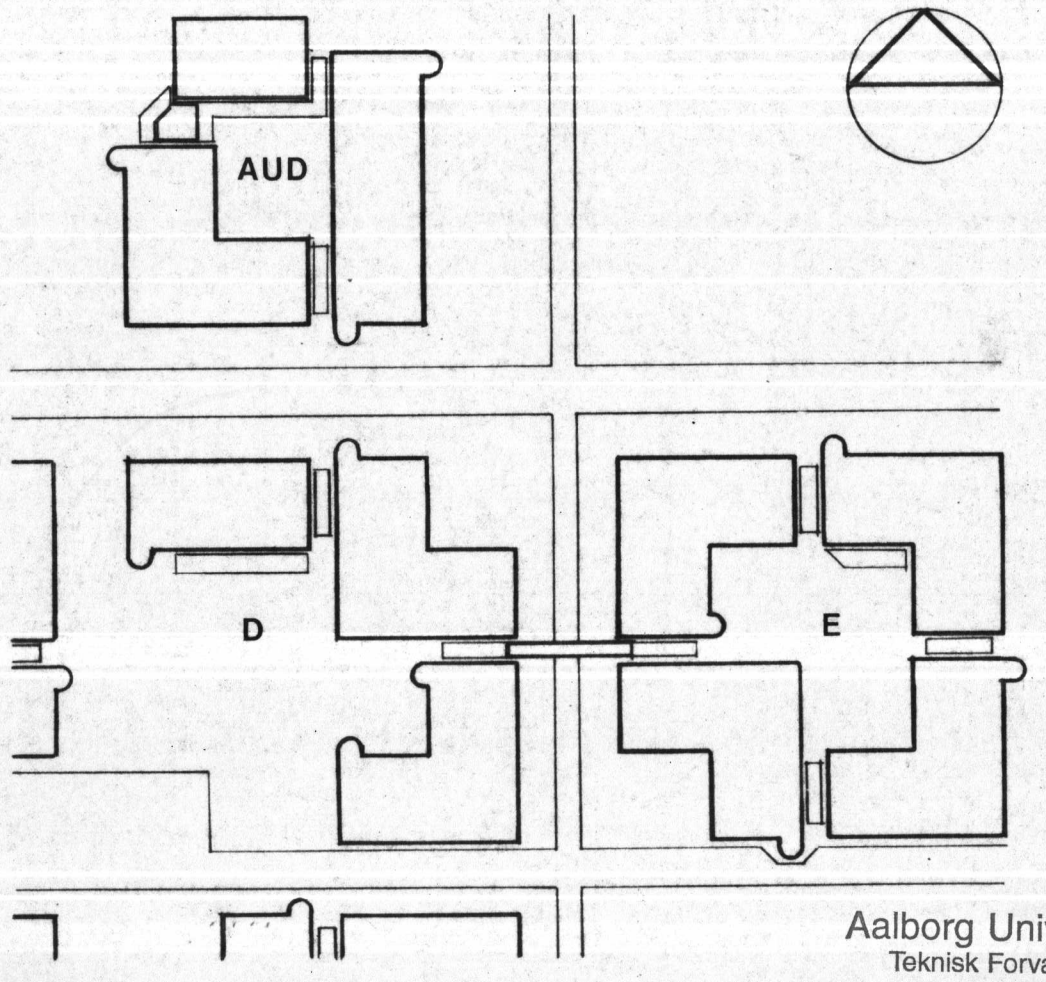

Aalborg Universitet
Teknisk Forvaltning

ALLE MÅL ER I MM

ORIGINAL KOPI

REV.	DATO	ÆNDRINGENS ART	SIGN.

AUC AALBORG UNIVERSITETSCENTER

6. BYGGEAFSNIT

SAG NR. 400.025.01

EMNE: Nedhængt gipsloft

MÅL : 1:20, 1:1

SIGN :

DATO: 01.06.88

TEGN. NR.

AR 6623

● ARKITEKTER HANS DALL & TORBEN LINDHARDTSEN A/S STJERNEGADE 5 3000 HELSINGØR TELF. 02 21 49 41
○ RÅDGIVENDE INGENIØRFIRMA CARL BRO A/S GRANSKOVEN 8 2600 GLOSTRUP TELF. 02 96 80 11
○ AUC BYGGEPLADSKONTORET FREDRIK BAJERS VEJ 300 9220 AALBORG Ø TELF. 08 15 93 11